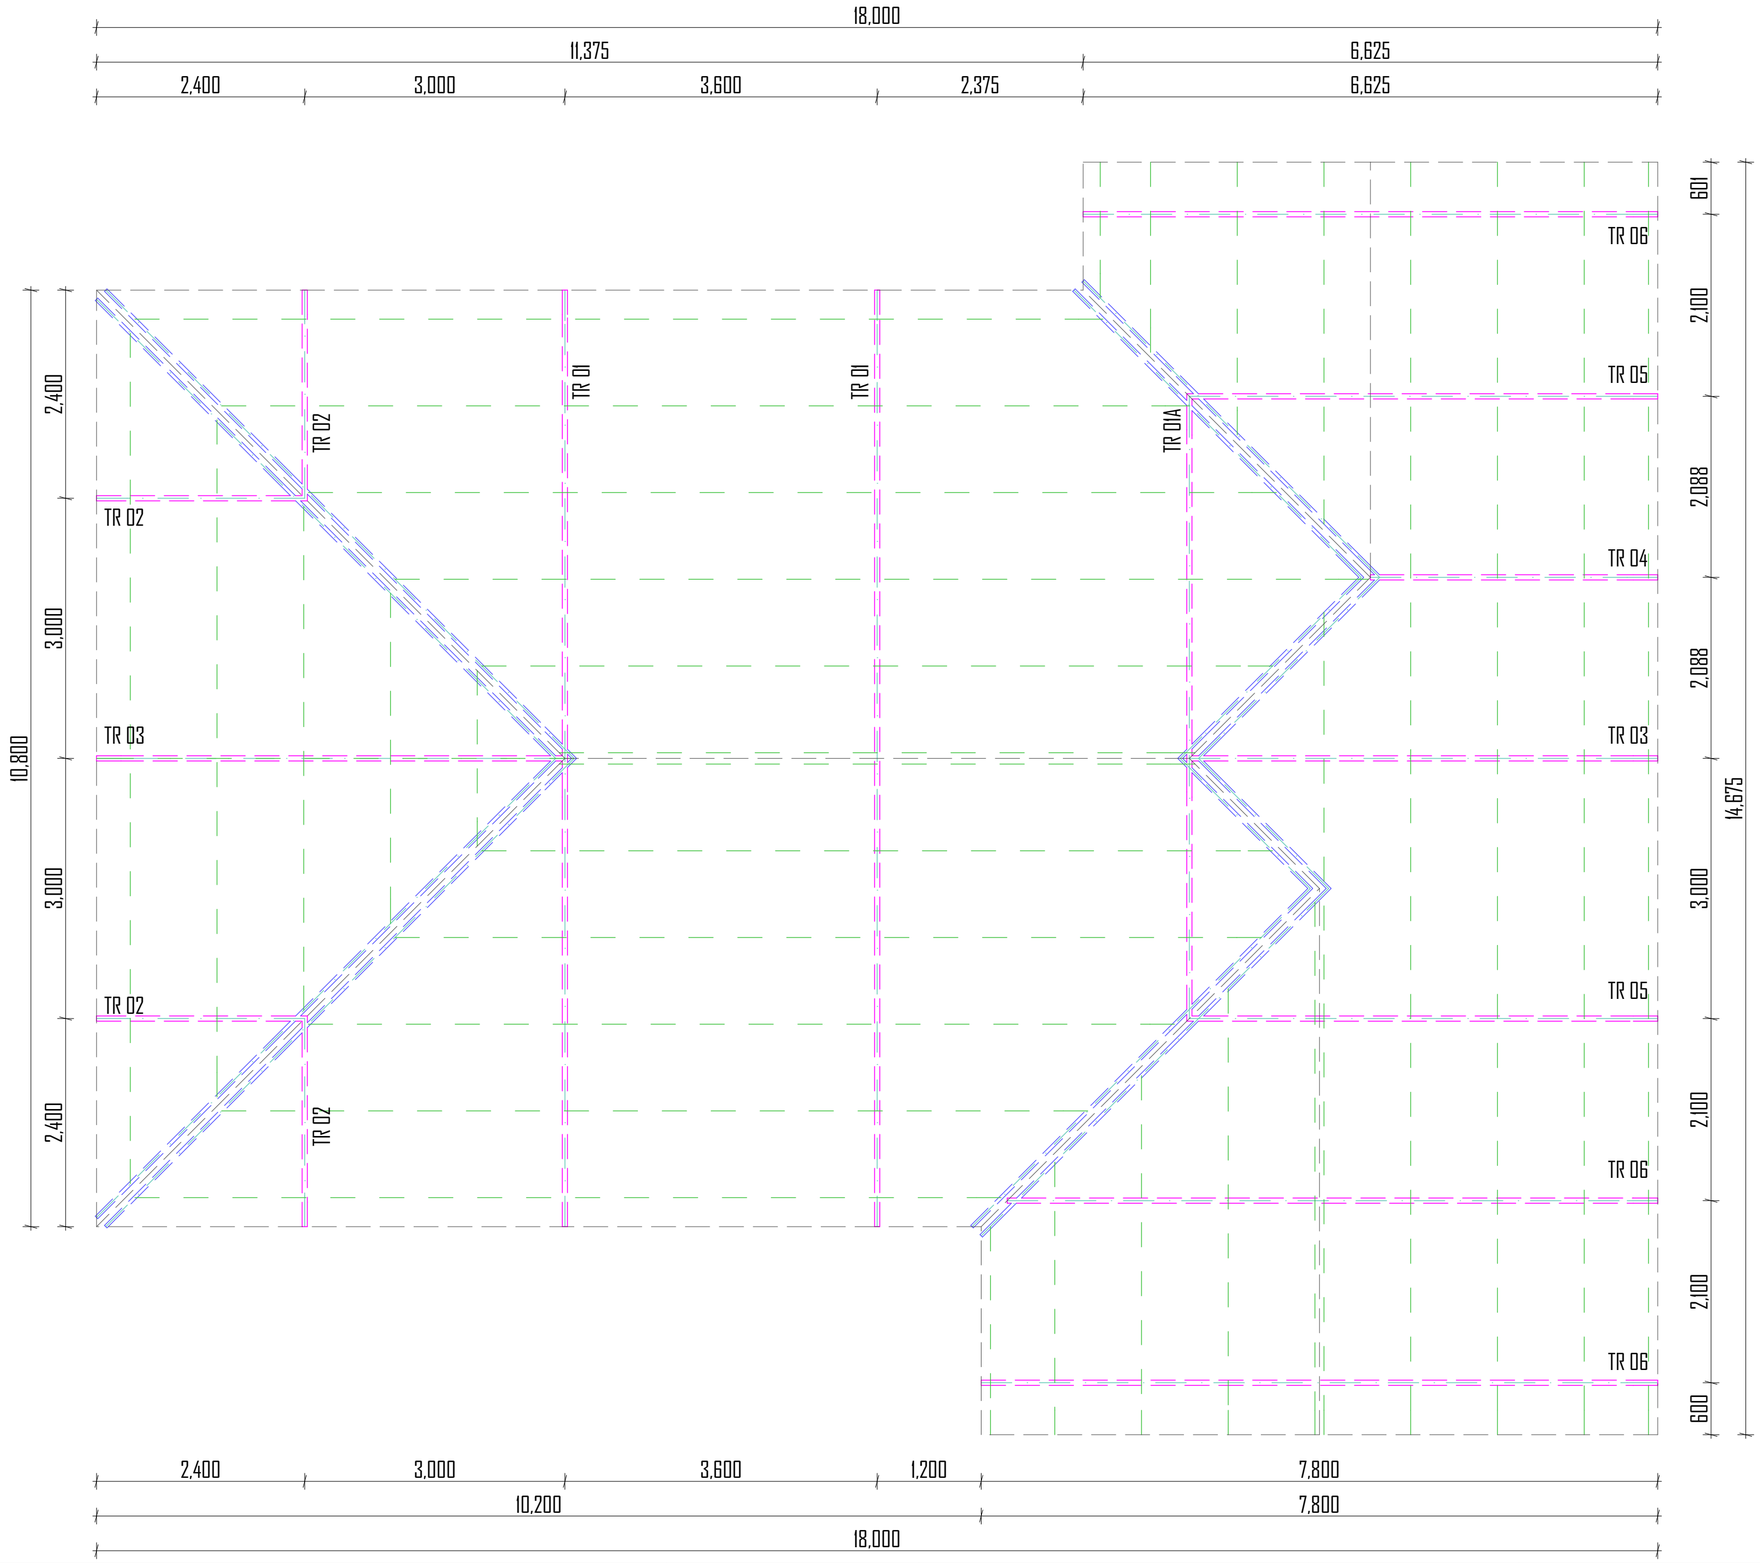

Drawing is copyright
Notes:

GENERAL NOTES:
Do not scale drawing. Use figured dimensions only. Overall dimensions take preference. All levels, heights and dimensions are to be checked on site before any work is put in hand. Any discrepancies, errors or omissions are to be reported to the Architect immediately.
The Contractor is responsible for the correct setting out of all relevant buildings, external and internal walls with particular reference to the relevant levels and setting-out points.

The drawing is property of Questafrica Limited. Copyright is reserved by them and the drawings is issued on the condition that it is not ammended, copied, reproduced, retained or disclosed to any unauthorised person, either wholly or in part without the written consent of Questafrica Limited.
No variation or instruction shall override the Contractor or Subcontractor's obligation to comply with the MINISTERIAL ORDER N° 04/Cab.M/015 OF 18/05/2015 DETERMINING URBAN PLANNING AND BUILDING REGULATIONS and ammendments thereto, as well as the by-laws of the relevant local municipality.
The appointed Structural Engineer to provide specifications and details for all reinforced foundation footings, concrete slabs, columns, beams and roof trusses.
All roofs to be in accordance with Rwanda Building Code (RBC)/British Standards(BS)

All floors to be in accordance RBC/BS (Refer to sections and
structural engineer's drawings.)
All walls to be in accordance with RBC/BS. (Refer to sections and
structural engineer's drawings.)
Unless specified otherwise, provide brickforce for every fourth course in all external and internal walls and for every course for four courses above all doors, windows and openings.
The appointed Structural Engineer to provide specifications and details for all reinforced foundation footings, concrete slabs, columns, beams and roof trusses.
Provide Rwanda Standards Board(RSB) approved DPM under all surface beds in
accordance with RBC/BS.

Provide RSB approved DPC's, whether or not these are indicated on the drawings, to all external walls at each floor, beam and parapet level, and to all windows, grilles and openings. Provide stepped DPC's to all cavity walls.
All glazing to be in accordance RBC/BS

PLUMBING AND DRAINAGE NOTES:
All plumbing and drainage work is to be designed and installed by the relevant Subcontractor and is to comply with BS as well as the relevant Local
Authority Bye-laws, regulations and requirements.
Plumbing and drainage indicated on the drawing is schematic only.
Provide IE's to all bends and junctions with suitable markers at ground level. Minimum falls to soil pipes to be 1:60. Provide approved reseal traps to all waste fittings. IE's to waste pipes to be fully accessible.

Provide RE's to the head of all runs, and to any run exceeding 25m in length
All drainage passing under buildings or footings are to be encased in concrete in accordance with the relevant Local Authority Bye-laws.
All material to be RBS approved throughout.

Client's signature

Architect's signature

REVISIONS

DATE	REVISION	CODE	INITIATED BY

Project;
KIBEHO, MUNINI TEA ESTATES PROJECT

Project adress:
NYARUGURU

Issue type: **Construction drawings**

Unilever

UNILEVER TEA -RWANDA

Drawing Title: **G.H ROOF STRUCTURAL LAYOUT PLAN**

Designed by: NDOSA BUILD Ltd

Scale: **As stated [A2]**

Drawn by: K.O

Checked by: U.J

Date: 05/02/2018

Drawing number
31

REV No.

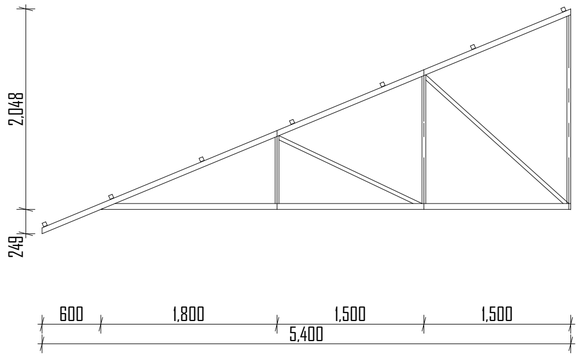

TRUSS TR 03
External members .R.H.S 60X40X3 mm
Internal members S.H.S 40X40X3 mm
Purlins S.H.S 40X40X3 MM
2 Nos Thus

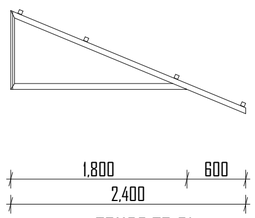

TRUSS TR 01
External members .R.H.S 60X40X3 mm
Internal members S.H.S 40X40X3 mm
4 Nos Thus

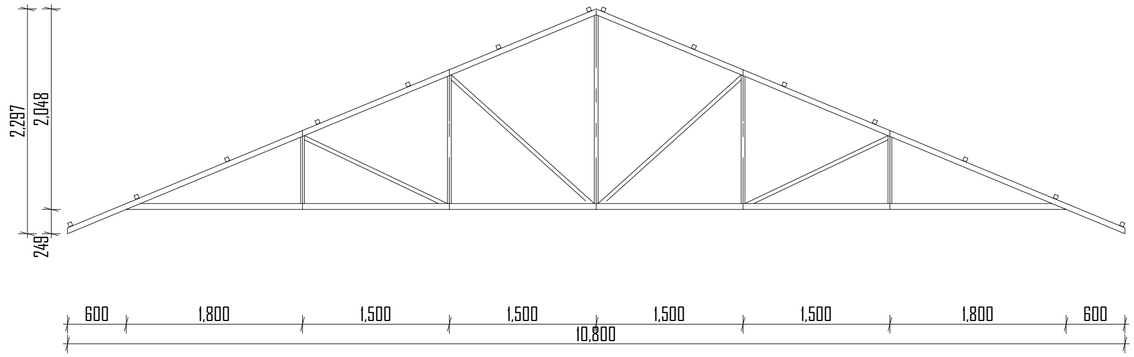

TRUSS TR 01
External members .R.H.S 60X40X3 mm
Internal members S.H.S 40X40X3 mm
Purlins S.H.S 40X40X3 MM
2 Nos Thus

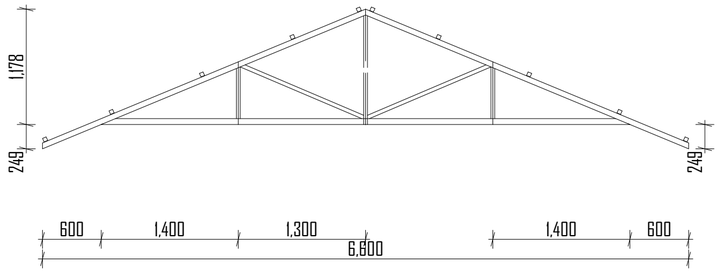

TRUSS TR 06
External members .R.H.S 60X40X3 mm
Internal members S.H.S 40X40X3 mm
2 Nos Thus

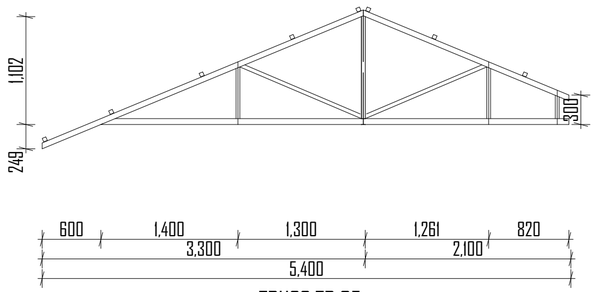

TRUSS TR 05
External members .R.H.S 60X40X3 mm
Internal members S.H.S 40X40X3 mm
2 Nos Thus

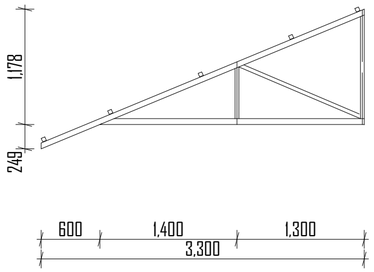

TRUSS TR 04
External members .R.H.S 60X40X3 mm
Internal members S.H.S 40X40X3 mm
1 Nos Thus

Drawing is copyright
Notes:

GENERAL NOTES:
Do not scale drawing. Use figured dimensions only.
Overall dimensions take preference. All levels, heights and dimensions are to be checked on site before any work is put in hand. Any discrepancies, errors or omissions are to be reported to the Architect immediately.
The Contractor is responsible for the correct setting out of all relevant buildings, external and internal walls with particular reference to the relevant levels and setting-out points.

The drawing is property of Questafrica Limited. Copyright is reserved by them and the drawings is issued on the condition that it is not ammended, copied, reproduced, retained or disclosed to any unauthorised person, either wholly or in part without the written consent of Questafrica Limited.
No variation or instruction shall override the Contractor or Subcontractors obligation to comply with the MINISTERIAL ORDER N° 04/Cab.M/015 OF 18/05/2015 DETERMINING URBAN PLANNING AND BUILDING REGULATIONS and ammendments thereto, as well as the by-laws of the relevant local municipality.
The appointed Structural Engineer to provide specifications and details for all reinforced foundation footings, concrete slabs, columns, beams and roof trusses.
All roofs to be in accordance with Rwanda Building Code (RBC)/British Standards(BS)

All floors to be in accordance RBC/BS (Refer to sections and
structural engineer's drawings.)
All walls to be in accordance with RBC/BS. (Refer to sections and
structural engineer's drawings.)
Unless specified otherwise, provide brickforce for every fourth course in all external and internal walls and for every course for four courses above all doors, windows and openings.
The appointed Structural Engineer to provide specifications and details for all reinforced foundation footings, concrete slabs, columns, beams and roof trusses.
Provide Rwanda Standards Board(RSB) approved DPM under all surface beds in
accordance with RBC/BS.

Provide RSB approved DPC's, whether or not these are indicated on the drawings, to all external walls at each floor, beam and parapet level, and to all windows, grilles and openings. Provide stepped DPC's to all cavity walls.
All glazing to be in accordance RBC/BS

PLUMBING AND DRAINAGE NOTES:
All plumbing and drainage work is to be designed and installed by the relevant Subcontractor and is to comply with BS as well as the relevant Local
Authority Bye-laws, regulations and requirements.
Plumbing and drainage indicated on the drawing is schematic only.
Provide IE's to all bends and junctions with suitable markers at ground level. Minimum falls to soil pipes to be 1:60. Provide approved reseal traps to all waste fittings. IE's to waste pipes to be fully accessible.

Provide RE's to the head of all runs, and to any run exceeding 25m in length.
All soil pipes passing under buildings or footings are to be encased in concrete in accordance with the relevant Local Authority Bye-laws.
All material to be RBS approved throughout.

Client's signature

Architect's signature

REVISIONS

DATE	REVISION	CODE	INITIATED BY

Project;
KIBEHO, MUNINI TEA ESTATES PROJECT

Project adress:
NYARUGURU

Issue type: **Construction drawings**

UNILEVER TEA -RWANDA

Drawing Title: **STEEL TRUSS SECTIONS**

Designed by: NOOSA BUILD Ltd

Scale: **As stated [A2]**

Drawn by: K.O

Checked by: U.J

Date: 05/02/2018

Drawing number
32

REV No.